

LEGENDA OBJEKTŮ A PŘÍPOJOK INŽINIERSKÝCH SIETÍ:

RCh	REKREAČNÁ CHATA-CHATA AMÉLIA
SP	SPEVNENÉ PLOCHY
AŠ	ARMATÚRNA ŠACHTA
Ž	ŽUMPA
Š	REVÍZNA KANALIZAČNÁ ŠACHTA PLASTOVÁ o 400mm
S	VŔTANÁ STUDŇA
	PŘÍPOJKA KANALIZÁCIE-PVC DN 160
	PŘÍPOJKA VODY-PE D 40
	HRANICE POZEMKOV

POZNÁMKA PODROBNÉ ZAKRESLENIE JEDNOTLIVÝCH PŘÍPOJOK SIETÍ
SÚ SPRACOVANÉ V PD - ELEKTRIKA, ZDRAVOTECHNIKA, PLYN



Kreslil	Ing. Radoslav Kandrik		
Vypracoval	Ing. Radoslav Kandrik		
Vedúci projektant	Ing. Radoslav Kandrik		
Zodpovedný projektant	Ing. Radoslav Kandrik		
Investor	Ing. Ján Popadák Hlavná 194/5 076 62 Parchovany	Generálny projektant R2R engineering s.r.o. KUKUČINOVA 710, Kysucké Nové Mesto SLOVAK REPUBLIC Tel.: +421 903 511 558 E-mail: rkandrik13@gmail.com	
Miesto	Homý Vadičov, PARC.Č.ČKN 1977/3 (1977/6-vznikne nová parcela podľa GP)(LV č. 2566)		Stupeň PSP-DOKUMENTÁCIA PRE STAVEBNÉ POVOLENIE
Stavba	REKREAČNÁ CHATA-CHATA AMELIA		Archívne číslo
			250DS05-01
			ID projektu
Názov	SITUÁCIA		Dátum
			09/2025
			Formát
			2xA4
		Mierka	1: 250
		Číslo výkresu	01

II
1977/2


1169000 + 433150

2694

II
1987/2

II
1983

1169050 + 433150

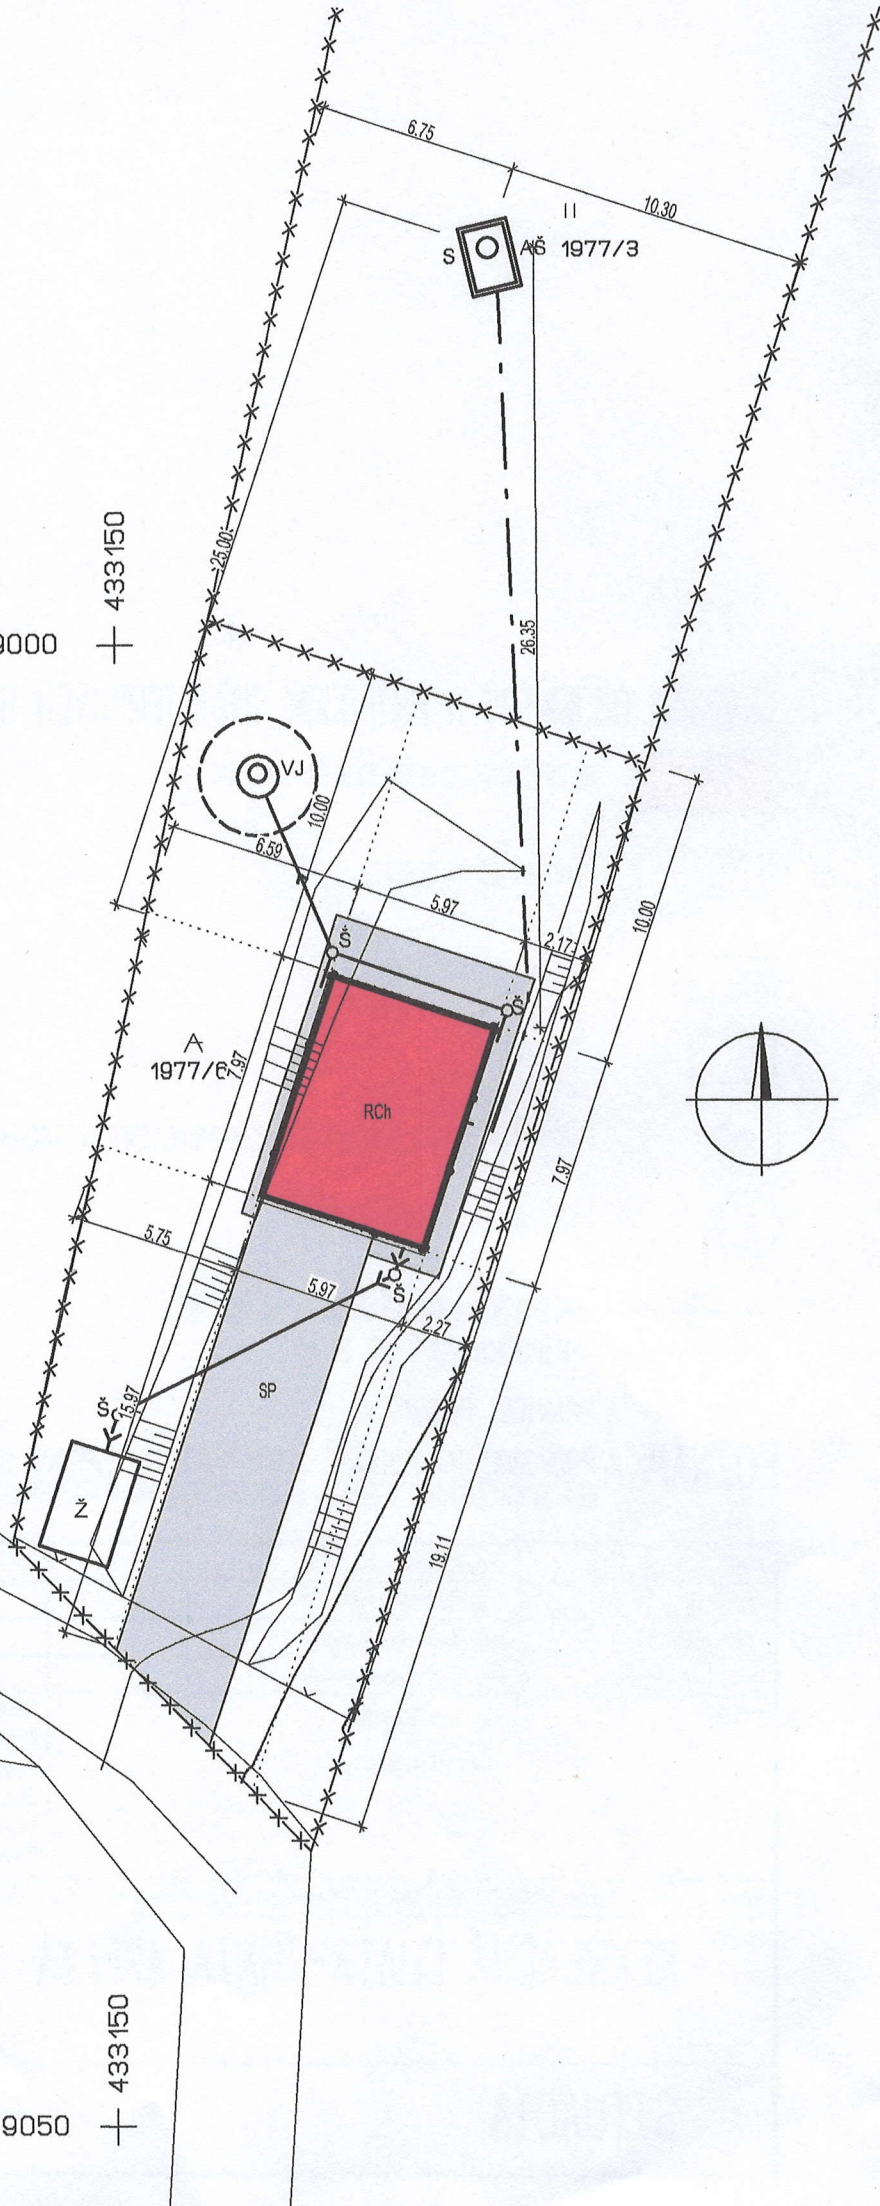

pouhá cesta