

LEGENDA MATERIÁLOV



LEGENDA

- F1 - CERTIFIKOVANÝ KONTAKTNÝ ZATEPLOVACÍ SYSTÉM (ETICS) V SOKLOVEJ ČASTI NA BÁZE XPS - IZOLANT DOSKY Z EXTRUDOVANÉHO POLYSTYRÉNU, HRÚBKA 200mm
 - V ČASTI NAD TERÉNOM ZHOTOVIŤ SIEŤKU+LEPIDLO+PENETRAČNÝ NÁTER, MARMOLIT
 - SUTERÉNNE MURIVO OČISTIŤ, VYSPRAVIŤ (CCA 50%) A ZHOTOVIŤ NOVÚ HYDROIZOLAČNÚ VRSTVU 1xCEMIX 1K, SPOJENIE JESTVUJÚCEJ IZOLÁCIE S NOVOU STIERKOU DILATAČNÝM PÁSMOM PODĽA TECH. LISTU VÝROBCU
- F2 - CERTIFIKOVANÝ KONTAKTNÝ ZATEPLOVACÍ SYSTÉM NA BÁZE MINERÁLNEJ VLNY-ZATEPLENIE FASÁDY, HRÚBKA 200mm, DEKLAROVANÝ SÚČINITEL TEPELNEJ VODIVOSTI (max. 0,035 W/(m.K), POVRCHOVÁ ÚPRAVA - FAREBNÉ RIEŠENIE URČÍ INVESTOR
- F3 - CERTIFIKOVANÝ KONTAKTNÝ ZATEPLOVACÍ SYSTÉM NA BÁZE MINERÁLNEJ VLNY-ZATEPLENIE OSTENÍ A NADPRAŽÍ OKIEN, VSTUPNÝCH DVERÍ, HRÚBKA 30mm, DEKLAROVANÝ SÚČINITEL TEPELNEJ VODIVOSTI (max. 0,035 W/(m.K), POVRCHOVÁ ÚPRAVA - FAREBNÉ RIEŠENIE URČÍ INVESTOR
- O1 - MONTÁŽ NOVÝCH OKIEN, INTERIEROVÝCH A EXTERIEROVÝCH PARAPETOV - PARAPRT POPLASTOVANÝ PLECH V ODTIENI PRÍSLUŠNÉHO OKNA (VIĎ. VÝPIS OKIEN A DVERÍ)
- D1 - MONTÁŽ NOVÝCH DVERÍ (VIĎ. VÝPIS OKIEN A DVERÍ)
- DI1 - MONTÁŽ NOVÝCH INT.DVERÍ (VIĎ. VÝPIS OKIEN A DVERÍ)
- Z - ZÁBRADLIE
- Z2 - MONTÁŽ NOVÝCH PODODKVAPOVÝCH ŽĽABOV, DAŽĎOVÝCH ZVODOV
- C - MONTÁŽ PLNÉHO SÁDROKARTÓNOVÉHO PODHLADU
- K - VÝSPRAVKA KOMÍNA (LEPIACA MALTA+SKLOTEXTILNÁ MRIEŽKA+MOZAIKOVÁ OMIETKA)
- B2 - NOVÉ PODBITIE STRECHY OSB DOSKA HR. 25mm + TEPELNÁ IZOLÁCIA Z MINERÁLNEJ VLNY HR. 30mm SIEŤKA+LEPIDLO-POVRCHOVÁ ÚPRAVA SILIKÓNOVÁ OMIETKA
- S2 - MONTÁŽ NOVEJ KRYTINY, LATOVANIA, FÓLIE (VIĎ. SKLADBA STRECHY)
- P1 - REALIZÁCIA NOVÝCH PODLAHOVÝCH VRSTIEV (VIĎ. SKLADBY PODLÁH)
- P3 - REALIZÁCIA NOVÝCH NÁŠĽAPNÝCH PODLAHOVÝCH VRSTIEV (VIĎ. SKLADBY PODLÁH)

POZNÁMKA:

- #1 Tento dokument je originál a jeho kopírovanie je trestné.
- #2 Všetky zmeny v projektoch treba prekonzultovať s HIP.
- #3 Všetky rozmery je nutné domerať priamo na stavbe. Rozmery sú kótované bez omietok.

±0,000 = 487 m.n.m.

Názov stavby : STAVEBNÉ ÚPRAVY MATERSKEJ ŠKOLY V HORNOM VADIČOVE č.515

LIMAT REALITY & BUILDING

Generálny projektant : LIMAT Reality&Building, s.r.o.

Zodpovedný projektant :		Vedúci projektant : Matúš Lipták		Dátum :	02 / 2024
Ing. Miroslav Moravec		Vypracoval/a : Ing. Renáta Čavajdová			
Investor : obec Horný Vadičov				Mierka :	1:100
Miesto stavby : obec Horný Vadičov		Okres : Kysucké nové Mesto		Formát :	2xA4
Kat. územie : Horný Vadičov		Parc. číslo : 1954/2		Úroveň :	DSP
Časť : ARCH		Názov výkresu : POHLÁDY - NOVÝ STAV			

LEGENDA MATERIÁLOV

- BÚRACIE PRÁCE
- BÚRACIE PRÁCE
- PÔVODNÁ KONŠTRUKCIA
- RASTLÝ TERÉN

LEGENDA

- F

- PÔVODNÝ KONTAKTNÝ ZATEPLOVACÍ SYSTÉM – ZATEPLENIE FASÁDY, HRÚBKA 100mm
- O

- DEMONTÁŽ PÔVODNÝCH OKIEN, INTERÉROVÝCH A EXTERIÉROVÝCH PARAPETOV
- D

- DEMONTÁŽ PÔVODNÝCH DVERÍ
- DI

- DEMONTÁŽ PÔVODNÝCH INT.DVERNÝCH KRÍDEL
- Z1

- DEMONTÁŽ PÔVODNÝCH PODODKVAPOVÝCH ŽLABOV, DAŽĎOVÝCH ZVODOV
- B1

- DEMONTÁŽ PÔVODNÉHO PODBITIA STRECHY
- S1

- DEMONTÁŽ PÔVODNEJ KRYTINY A LATOVANIA (VIĎ. SKLADBA STRECHY)
- P

- ODSTRÁNENIE PÔVODNÝCH PODLAHOVÝCH VRSTIEV PO ŽELEZOBET. DOSKU
- P2

- ODSTRÁNENIE PÔVODNÝCH NÁŠLAPNÝCH PODLAHOVÝCH VRSTIEV

POZNÁMKA:

- #1 Tento dokument je originál a jeho kopírovanie je trestné.
- #2 Všetky zmeny v projektoch treba prekonzultovať s HIP.
- #3 Všetky rozmery je nutné domerať priamo na stavbe. Rozmery sú kótované bez omietok.

±0,000 = 487 m.n.m.

Názov stavby :

STAVEBNÉ ÚPRAVY MATERSKEJ ŠKOLY
V HORNOM VADIČOVE č.515



Generálny projektant : LIMAT Reality&Building, s.r.o.

Zodpovedný projektant :
Ing. Miroslav Moravec

Vedúci projektant : Matúš Lipták
Vypracoval/a : Ing. Renáta Čavajdová

Dátum : 02 / 2024

Investor : obec Horný Vadičov

Mierka : 1:100

Miesto stavby : obec Horný Vadičov | Okres : Kysucké nové Mesto

Formát : 2xA4

Kat. územie : Horný Vadičov | Parc. číslo : 1954/2


Úroveň : DSP

Časť :
ARCH


Názov výkresu :

POHLÁDY - STARÝ STAV


JUHOVÝCHODNÝ POHĽAD

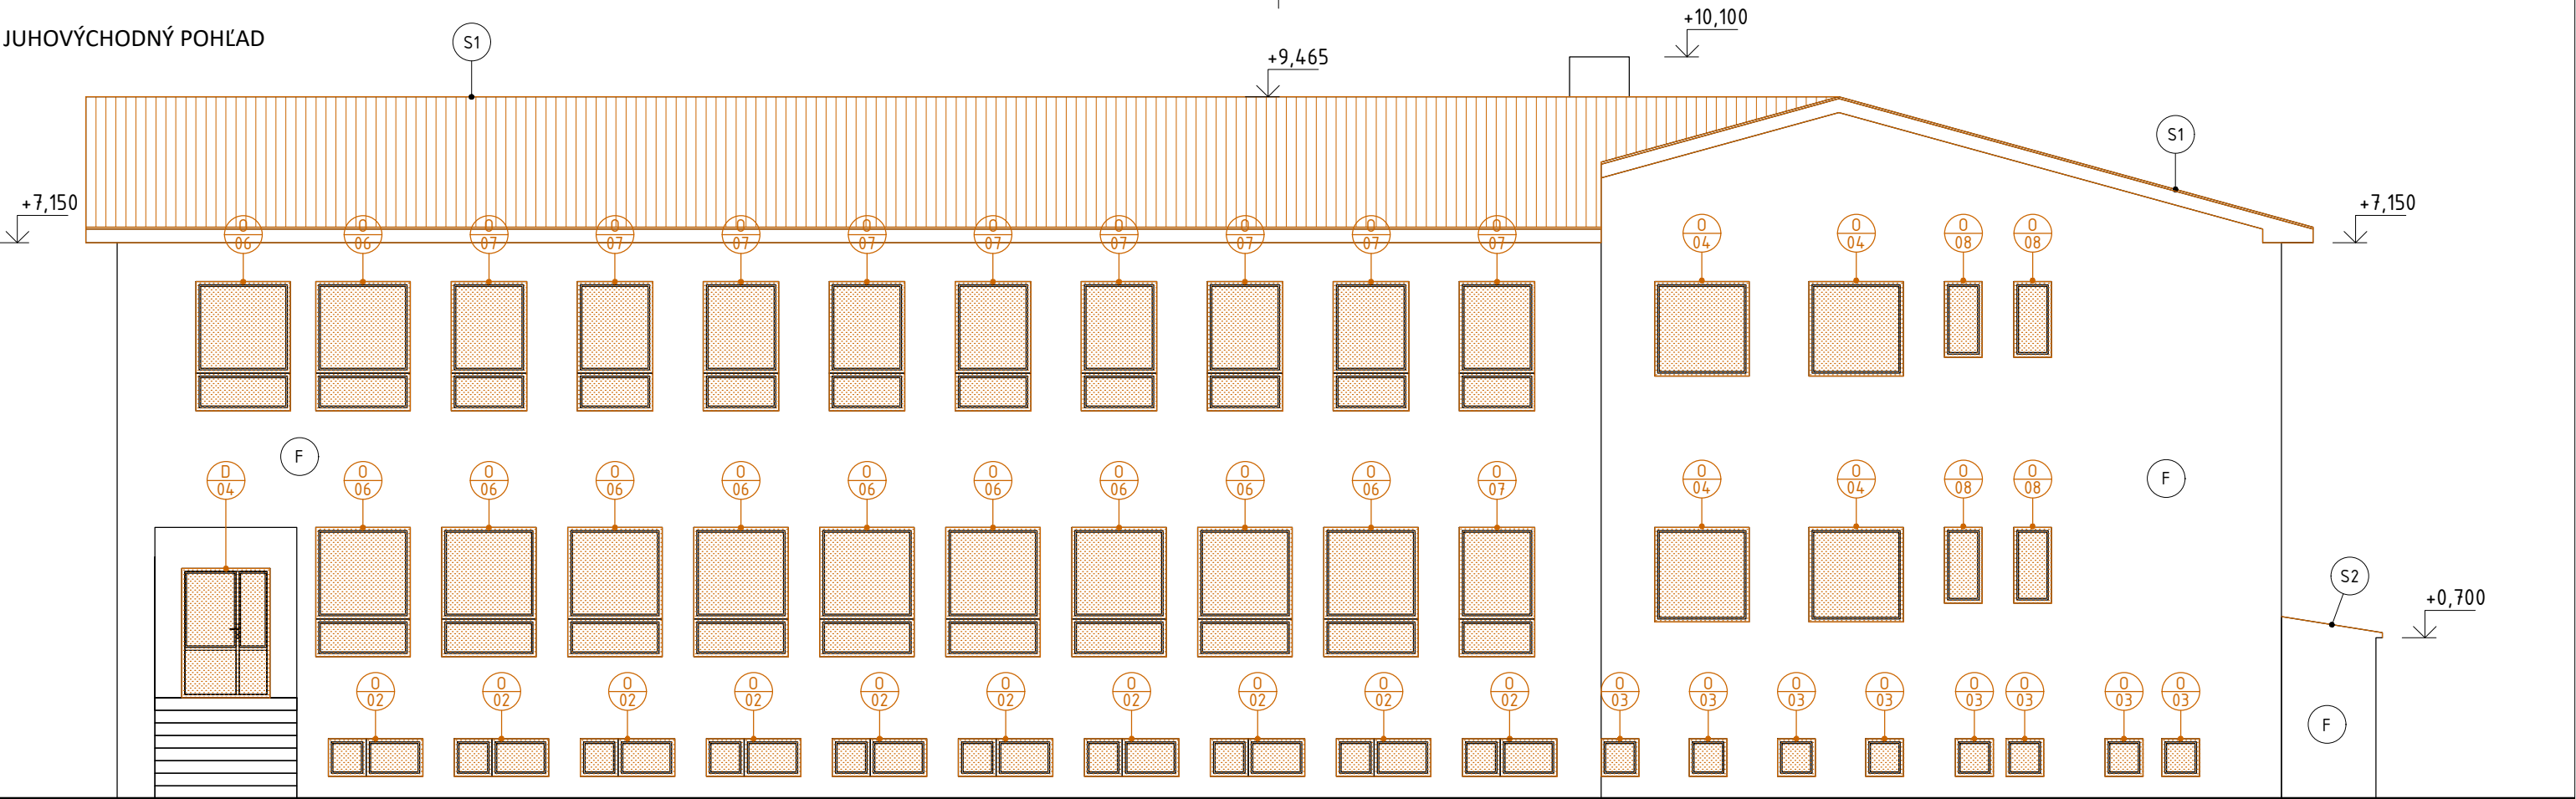

SEVEROZÁPADNÝ POHĽAD

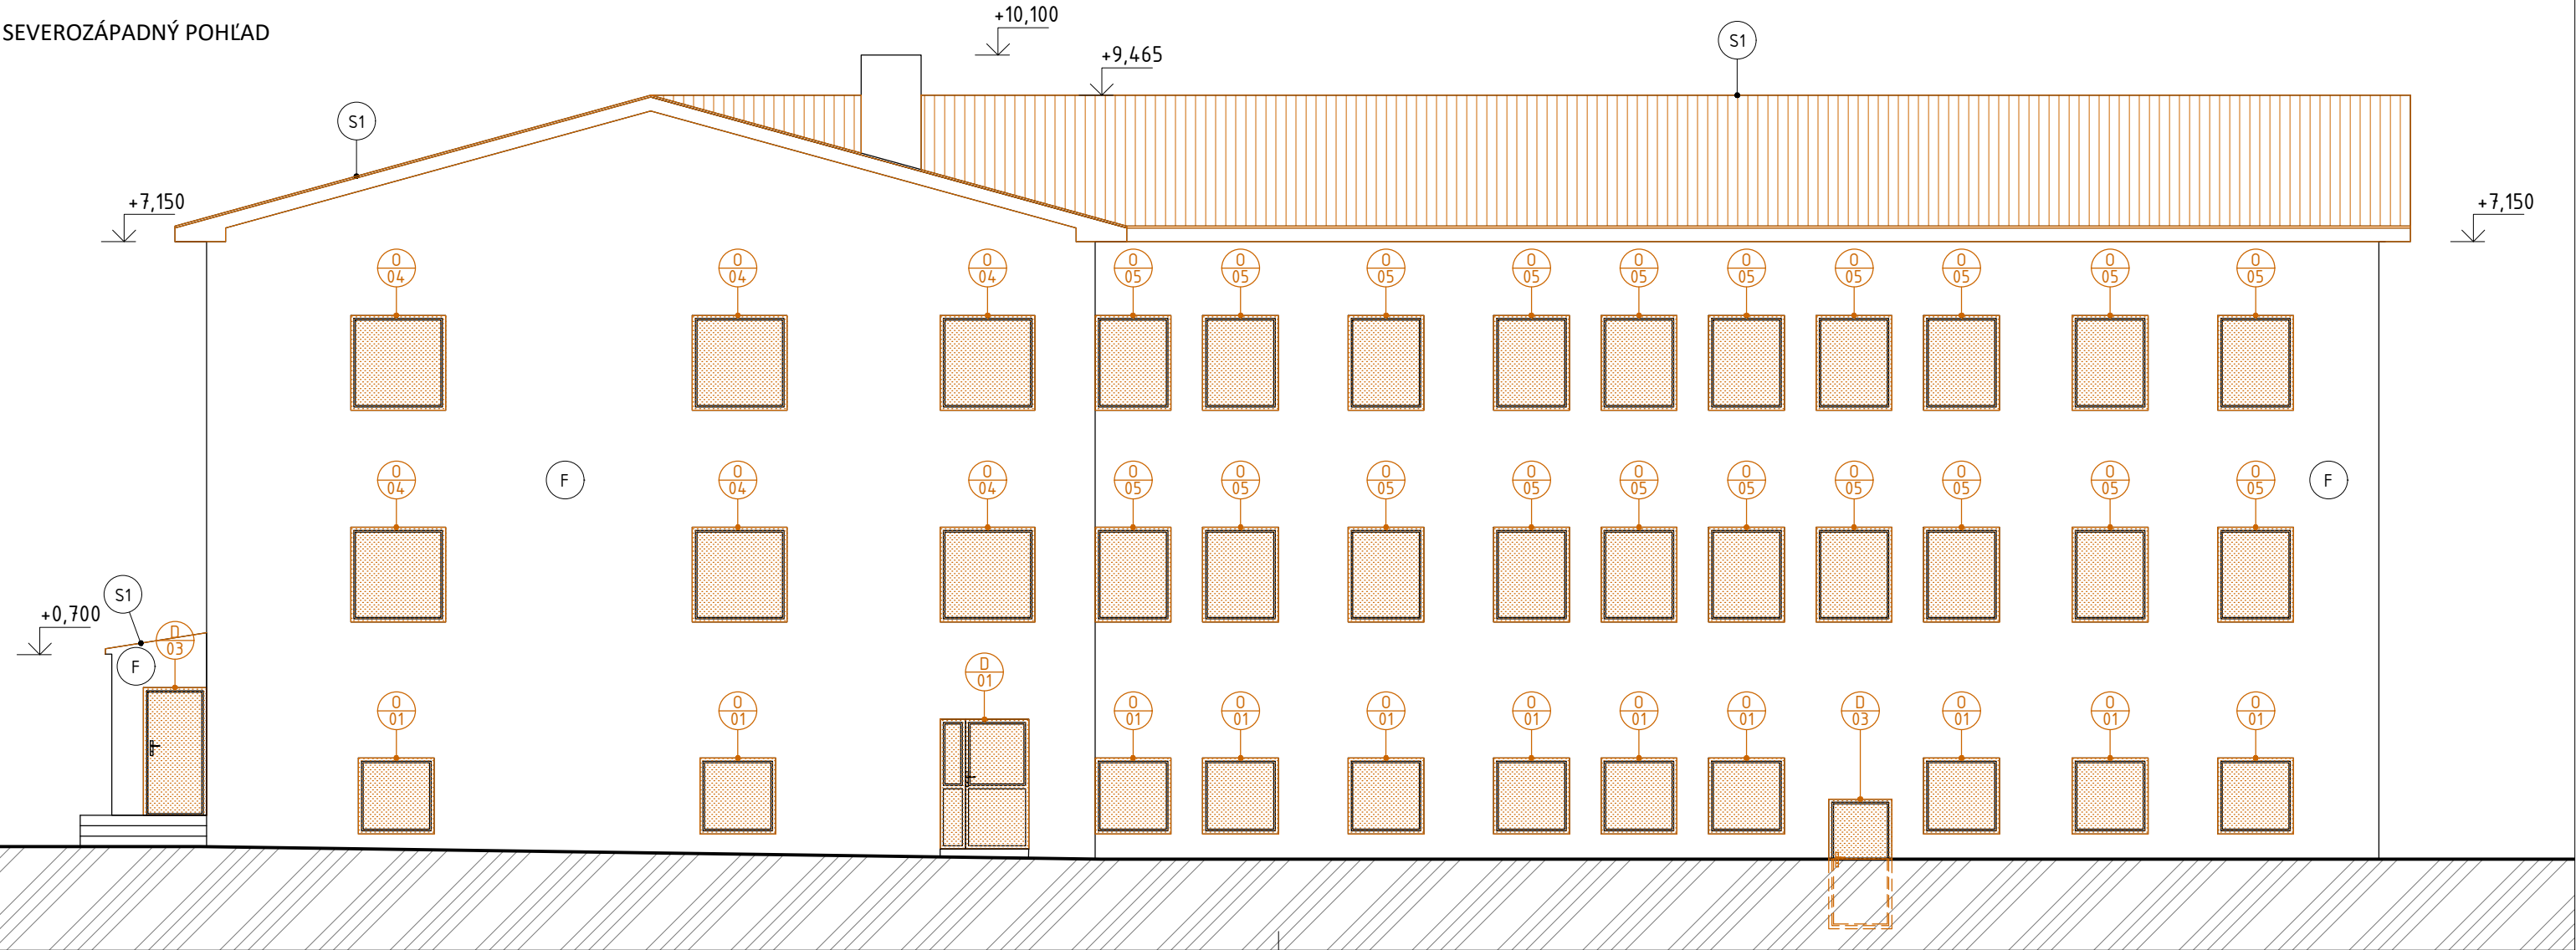

SEVEROVÝCHODNÝ POHĽAD

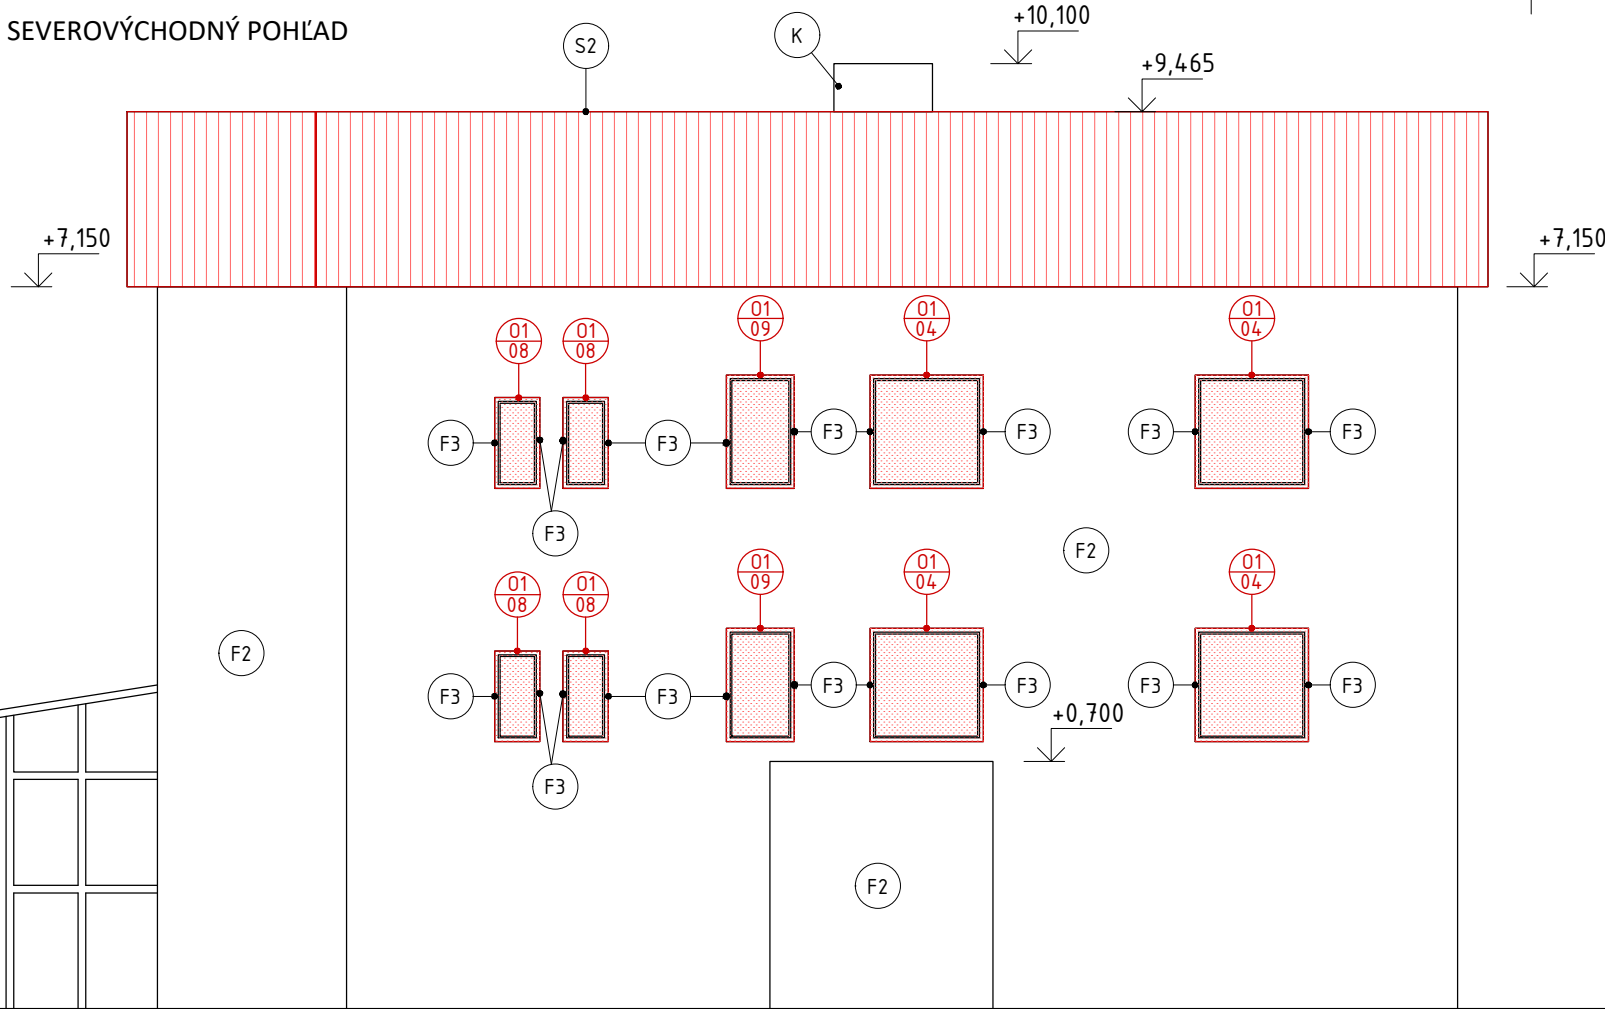


LEGENDA MATERIÁLOV

- NOVÉ PRÁCE
- NOVÉ PRÁCE
- PŮVODNÁ KONŠTRUKCIA
- RASTLÝ TERÉN

LEGENDA

- F1 - CERTIFIKOVANÝ KONTAKTNÝ ZATEPLOVACÍ SYSTÉM (ETICS) V SOKLOVEJ ČASTI NA BÁZE XPS - IZOLANT DOSKY Z EXTRUDOVANÉHO POLYSTYRÉNU, HRÚBKA 200mm
- V ČASTI NAD TERÉNOM ZHOTOVIŤ SIEŤKU+LEPIDLO+PENETRAČNÝ NÁTER, MARMOLIT
- SUTERÉNNE MURIVO OČISTIŤ, VYSPRAVIŤ (CCA 50%) A ZHOTOVIŤ NOVÚ HYDROIZOLAČNÚ VRSTVU 1xCEMIX 1K, SPOJENIE JESTVUJÚCEJ IZOLÁCIE S NOVOU STIERKOU DILATAČNÝM PÁSMOM PODĽA TECH. LISTU VÝROBCU
- F2 - CERTIFIKOVANÝ KONTAKTNÝ ZATEPLOVACÍ SYSTÉM NA BÁZE MINERÁLNEJ VLNY-ZATEPLENIE FASÁDY, HRÚBKA 200mm, DEKLAROVANÝ SÚČINITEĽ TEPELNEJ VODIVOSTI (max. 0,035 W/(m.K), POVRCHOVÁ ÚPRAVA - FAREBNÉ RIEŠENIE URČÍ INVEŠTOR
- F3 - CERTIFIKOVANÝ KONTAKTNÝ ZATEPLOVACÍ SYSTÉM NA BÁZE MINERÁLNEJ VLNY-ZATEPLENIE OSTENÍ A NADPRAŽÍ OKIEN, VSTUPNÝCH DVERÍ, HRÚBKA 30mm, DEKLAROVANÝ SÚČINITEĽ TEPELNEJ VODIVOSTI (max. 0,035 W/(m.K), POVRCHOVÁ ÚPRAVA - FAREBNÉ RIEŠENIE URČÍ INVEŠTOR
- O1 - MONTÁŽ NOVÝCH OKIEN, INTERIEROVÝCH A EXTERIEROVÝCH PARAPETOV - PARAPRT POPLASTOVANÝ PLECH V ODTIENI PRÍSLUŠNÉHO OKNA (VIĎ. VÝPIS OKIEN A DVERÍ)
- O1 - MONTÁŽ NOVÝCH DVERÍ (VIĎ. VÝPIS OKIEN A DVERÍ)
- D1 - MONTÁŽ NOVÝCH INT.DVERÍ (VIĎ. VÝPIS OKIEN A DVERÍ)
- Z - ZÁBRADLIE
- Z2 - MONTÁŽ NOVÝCH PODODKVAPOVÝCH ŽLABOV, DAŽĎOVÝCH ZVODOV
- C - MONTÁŽ PLNÉHO SÁDROKARTÓNOVÉHO PODHLADU
- K - VÝSPRAVKA KOMÍNA (LEPIACA MALTA+SKLOTEXTILNÁ MRIEŽKA+MOZAIKOVÁ OMIETKA)
- B2 - NOVÉ PODBITIE STRECHY OSB DOSKA HR. 25mm + TEPELNÁ IZOLÁCIA Z MINERÁLNEJ VLNY HR. 30mm SIEŤKA+LEPIDLO-POVRCHOVÁ ÚPRAVA SILIKÓNOVÁ OMIETKA
- S2 - MONTÁŽ NOVEJ KRYTINY, LATOVANIA, FÓLIE (VIĎ. SKLADBA STRECHY)
- P1 - REALIZÁCIA NOVÝCH PODLAHOVÝCH VRSTIEV (VIĎ. SKLADBY PODLÁH)
- P3 - REALIZÁCIA NOVÝCH NÁŠĽAPNÝCH PODLAHOVÝCH VRSTIEV (VIĎ. SKLADBY PODLÁH)

JUHOZÁPADNÝ POHĽAD

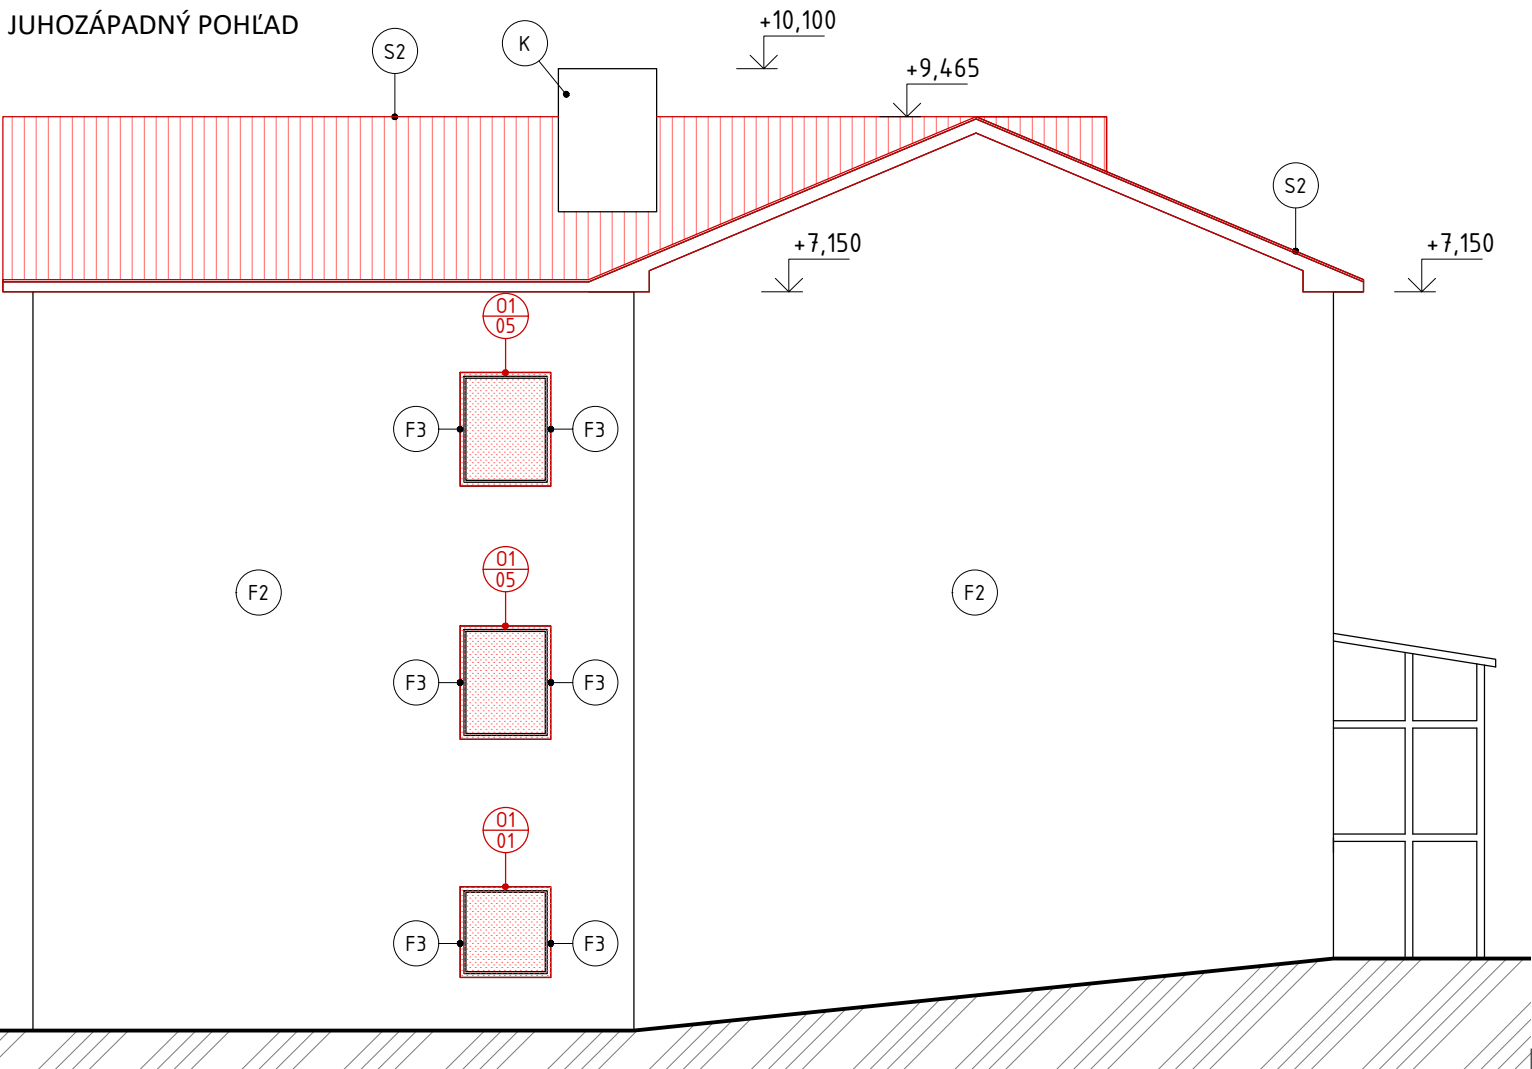

POZNÁMKA:

- #1 Tento dokument je originál a jeho kopírovanie je trestné.
- #2 Všetky zmeny v projektoch treba prekonzultovať s HIP.
- #3 Všetky rozmery je nutné domerať priamo na stavbe. Rozmery sú kótované bez omyetok.

±0,000 = 487 m.n.m.

Názov stavby : **STAVEBNÉ ÚPRAVY MATERSKEJ ŠKOLY
V HORNOM VADIČOVE č.515**

LIMAT
REALITY & BUILDING

Generálny projektant : LIMAT Reality&Building, s.r.o.

Zodpovedný projektant : Ing. Miroslav Moravec
Vedúci projektant : Matúš Lipták
Vypracoval/a : Ing. Renáta Čavajdová

Investor : obec Horný Vadičov

Miesto stavby : obec Horný Vadičov | Okres : Kysucké nové Mesto
Kat. územie : Horný Vadičov | Parc. číslo : 1954/2

Časť : ARCH
Názov výkresu :



POHĽADY - NOVÝ STAV

Dátum : 02 / 2024

Mierka : 1:100

Formát : 2xA4

Úroveň : DSP

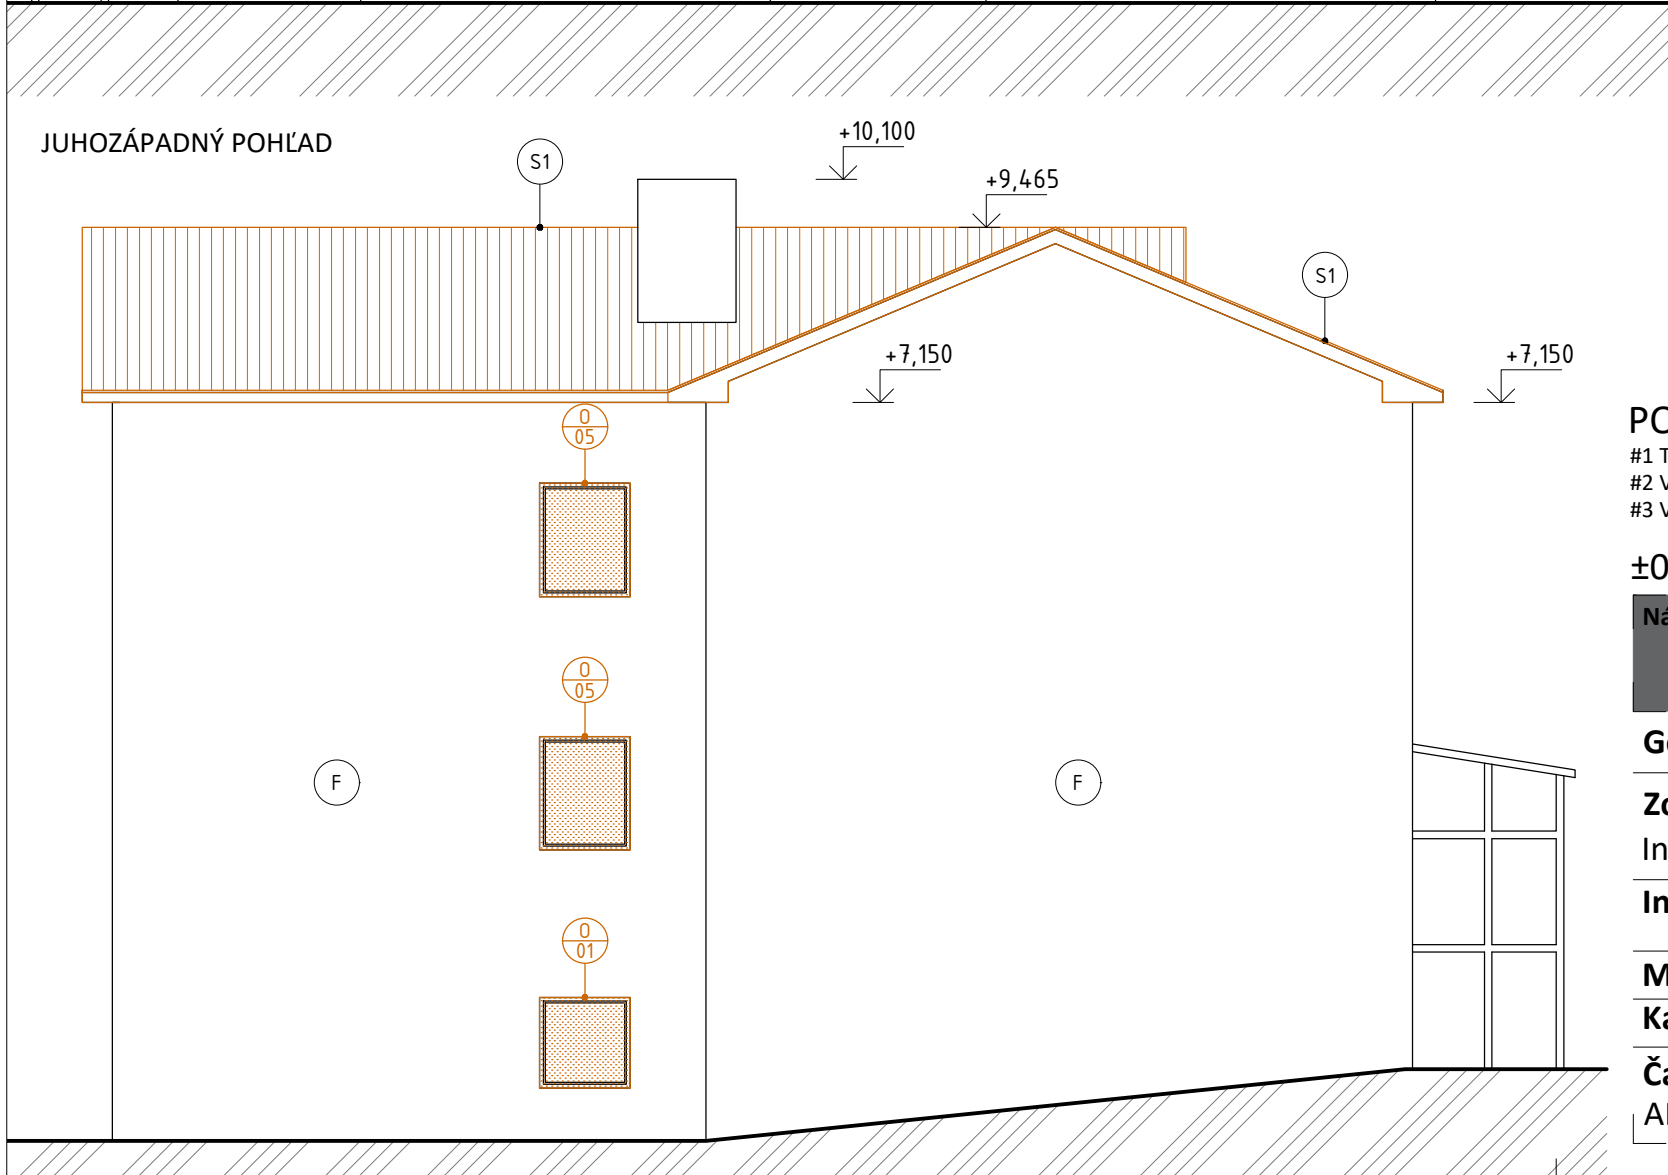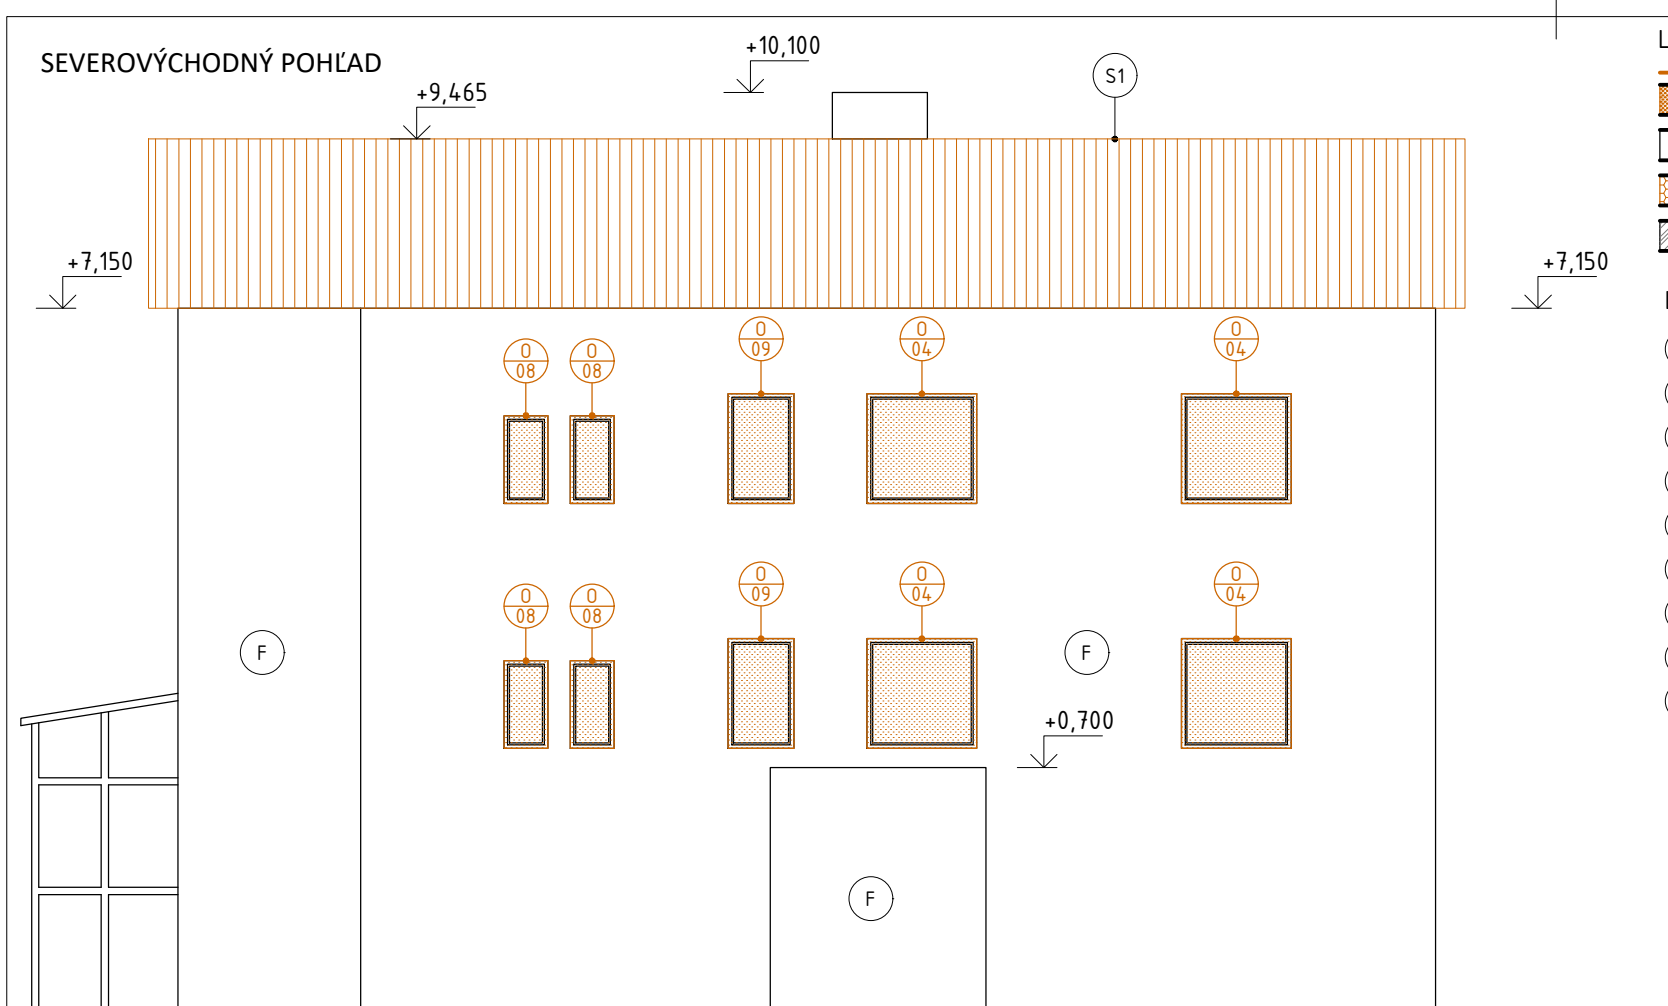

LEGENDA MATERIÁLOV

- BÚRACIE PRÁCE
- BÚRACIE PRÁCE
- PŮVODNÁ KONŠTRUKCIA
- TEPELNÁ IZOLÁCIA
- RASTLÝ TERÉN

LEGENDA

- F - PŮVODNÝ KONTAKTNÝ ZATEPLOVACÍ SYSTÉM - ZATEPLENIE FASÁDY, HRÚBKA 100mm
- O - DEMONTÁŽ PŮVODNÝCH OKIEN, INTERIÉROVÝCH A EXTERIÉROVÝCH PARAPETOV
- D - DEMONTÁŽ PŮVODNÝCH DVERÍ
- Di - DEMONTÁŽ PŮVODNÝCH INT.DVERNÝCH KRÍDEL
- Z1 - DEMONTÁŽ PŮVODNÝCH PODODKVAPOVÝCH ŽLABOV, DAŽĎOVÝCH ZVODOV
- B1 - DEMONTÁŽ PŮVODNÉHO PODBITIA STRECHY
- S1 - DEMONTÁŽ PŮVODNEJ KRYTINY A LATOVANIA (VIĎ. SKLADBA STRECHY)
- P - ODSTRÁNENIE PŮVODNÝCH PODLAHOVÝCH VRSTIEV PO ŽELEZOBET. DOSKU
- P2 - ODSTRÁNENIE PŮVODNÝCH NÁŠĽAPNÝCH PODLAHOVÝCH VRSTIEV

POZNÁMKA:

- #1 Tento dokument je originál a jeho kopírovanie je trestné.
- #2 Všetky zmeny v projektoch treba prekonzultovať s HIP.
- #3 Všetky rozmery je nutné domeriť priamo na stavbe. Rozmery sú kótované bez omietok.

±0,000 = 487 m.n.m.

Názov stavby : **STAVEBNÉ ÚPRAVY MATERSKEJ ŠKOLY
V HORNOM VADIČOVE č.515**

LIMAT
REALITY & BUILDING

Generálny projektant : LIMAT Reality&Building, s.r.o.

Zodpovedný projektant : Ing. Miroslav Moravec
Vedúci projektant : Matúš Lipták
Vypracoval/a : Ing. Renáta Čavajdová

Dátum : 02 / 2024

Investor : obec Horný Vadičov

Mierka : 1:100

Miesto stavby : obec Horný Vadičov | Okres : Kysucké nové Mesto

Formát : 2xA4


Kat. územie : Horný Vadičov | Parc. číslo : 1954/2

Úroveň : DSP

Časť :
ARCH

Názov výkresu :

POHĽADY - STARÝ STAV

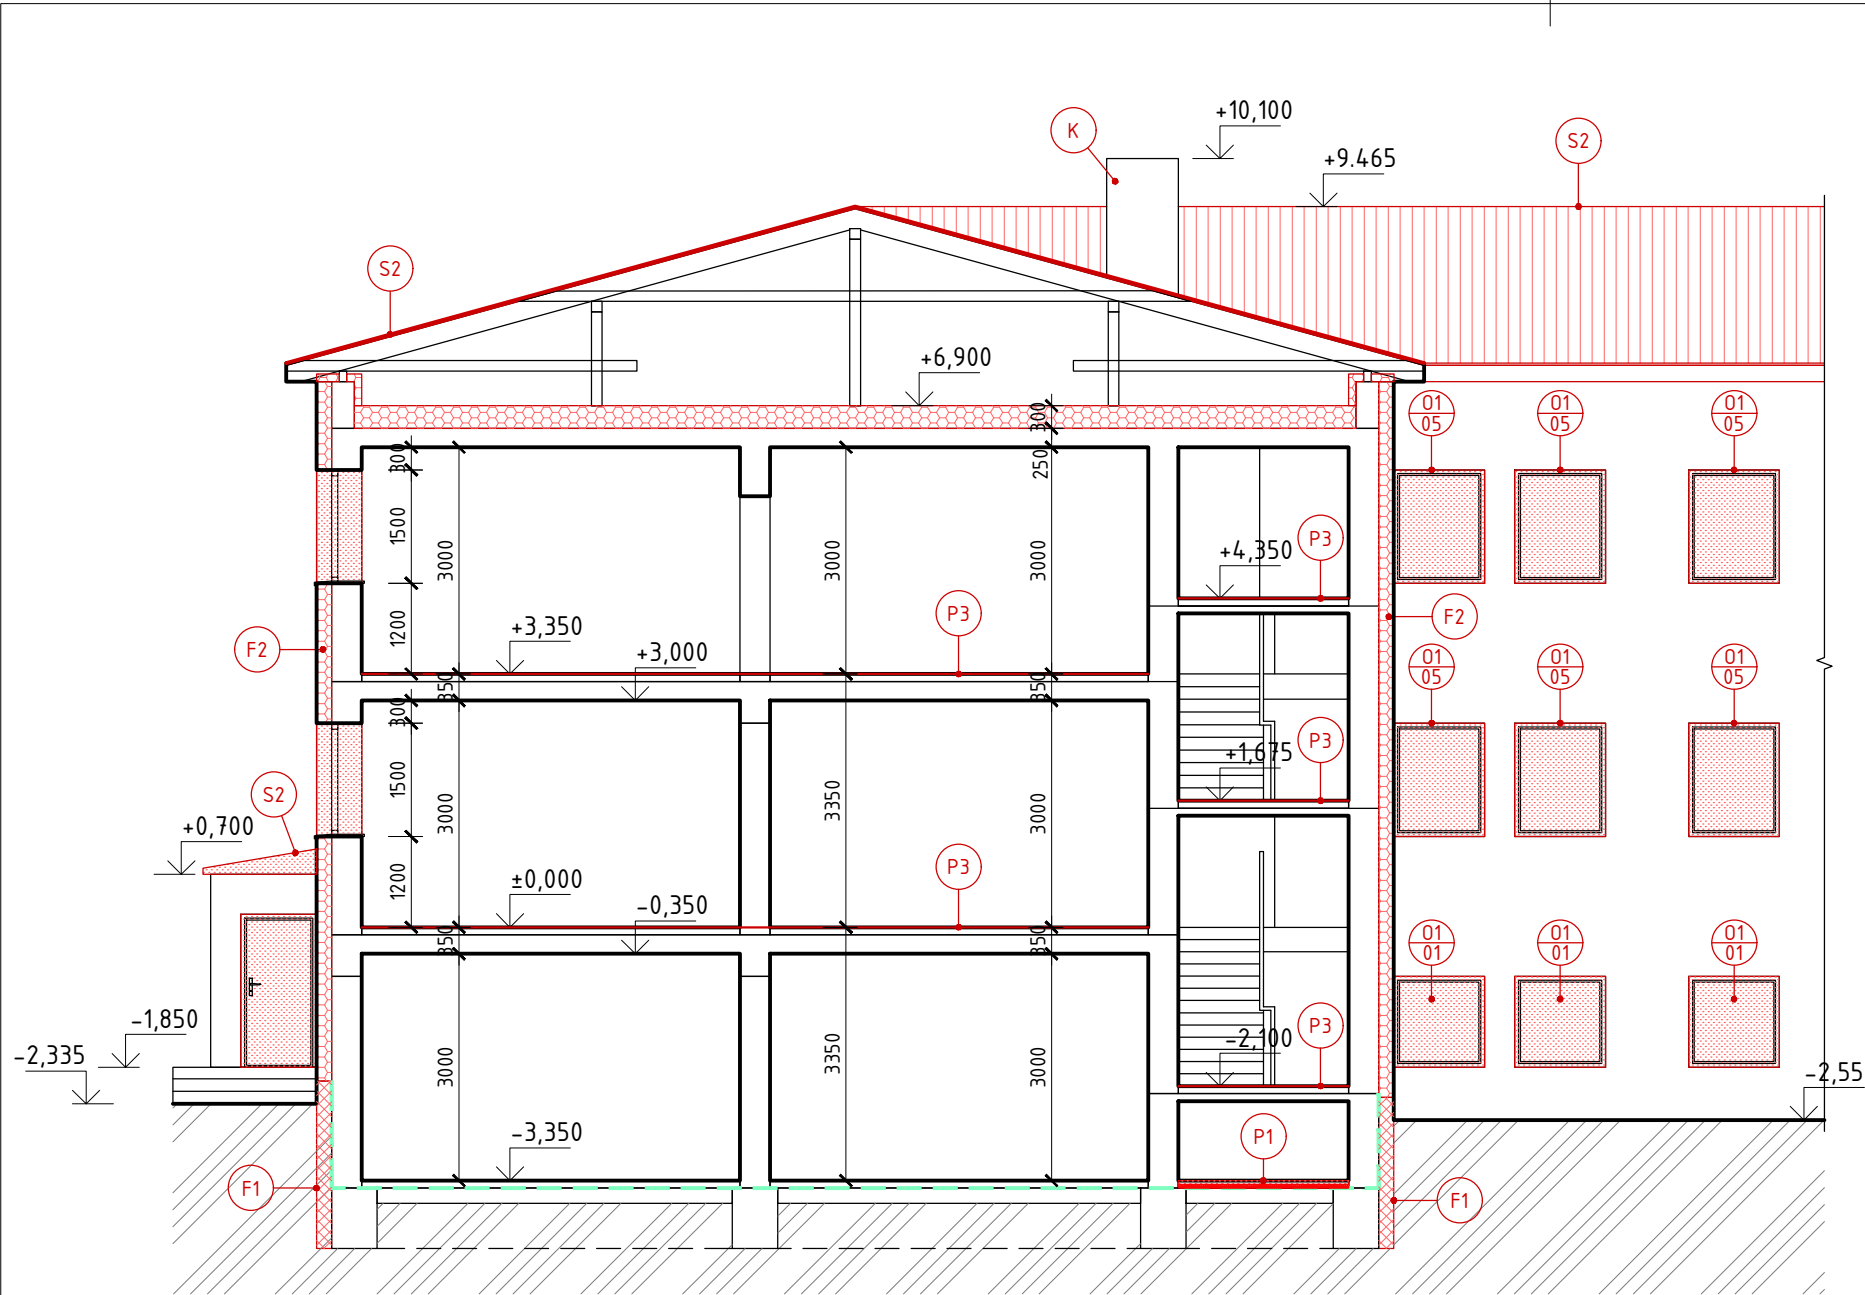

SKLADBY PODLÁH

- P1 - NÁŠLAPNÁ VRSTVA 8mm
- PODLAHOVÉ LEPIDLO 2mm
- BET. POTER 40mm
- PODLAHOVÝ POLYSTYRÉN 50 mm
- PODKLADNÝ BETÓN
- RASTLÝ TERÉN

- P3 - PVC LINOLEUM 2mm
- LEPIDLO POD PVC
- SAMONIVELIZAČNÝ POTER

SKLADBA STRECHY

- S2 - FALCOVANÝ PLECH
- PAROZÁBRANA
- PLNÝ ZÁKLUP hr. 25mm
- KONTRALATY
- PAROPRIEPUSTNÁ FÓLIA
- PÔVODNÝ KROV

LEGENDA

- F1 - CERTIFIKOVANÝ KONTAKTNÝ ZATEPLOVACÍ SYSTÉM (ETICS) V SOKLOVEJ ČASTI NA BÁZE XPS - IZOLANT DOSKY Z EXTRUDOVANÉHO POLYSTYRÉNU, HRÚBK 200mm
- V ČASTI NAD TERÉNOM ZHOTVIŤ SIEŤKU+LEPIDLO+PENETRAČNÝ NÁTER, MARMOLIT
- SUTERÉNNE MURIVO OČISTIŤ, VYSPRAVIŤ (CCA 50%) A ZHOTVIŤ NOVÚ HYDROIZOLAČNÚ VRSTVU 1xCEMIX 1K, SPOJENIE JESTVUJÚCEJ IZOLÁCIE S NOVOU STIERKOU DILATAČNÝM PÁSMOM PODĽA TECH. LISTU VÝROBCU
- F2 - CERTIFIKOVANÝ KONTAKTNÝ ZATEPLOVACÍ SYSTÉM NA BÁZE MINERÁLNEJ VLNY-ZATEPLENIE FASÁDY, HRÚBK 200mm, DEKLAROVANÝ SÚČINITEL TEPELNEJ VODIVOSTI (max. 0,035 W/(m.K), POVRCHOVÁ ÚPRAVA - FAREBNÉ RIEŠENIE URČÍ INVEŠTOR
- F3 - CERTIFIKOVANÝ KONTAKTNÝ ZATEPLOVACÍ SYSTÉM NA BÁZE MINERÁLNEJ VLNY-ZATEPLENIE OSTEŇÍ A NADPRAŽÍ OKIEN, VSTUPNÝCH DVERÍ, HRÚBK 30mm, DEKLAROVANÝ SÚČINITEL TEPELNEJ VODIVOSTI (max. 0,035 W/(m.K), POVRCHOVÁ ÚPRAVA - FAREBNÉ RIEŠENIE URČÍ INVEŠTOR
- O1 - MONTÁŽ NOVÝCH OKIEN, INTERIEROVÝCH A EXTERIEROVÝCH PARAPETOV - PARAPET POPLASTOVANÝ PLECH V ODTIENI PRÍSLUŠNÉHO OKNA (VIĎ. VÝPIS OKIEN A DVERÍ)
- D1 - MONTÁŽ NOVÝCH DVERÍ (VIĎ. VÝPIS OKIEN A DVERÍ)
- D11 - MONTÁŽ NOVÝCH INT.DVERÍ (VIĎ. VÝPIS OKIEN A DVERÍ)
- Z - ZÁBRADLIE
- Z2 - MONTÁŽ NOVÝCH PODODKVAPOVÝCH ŽLABOV, DAŽĎOVÝCH ZVODOV
- C - MONTÁŽ PLNÉHO SÁDROKARTÓNEHO PODHLADU
- K - VÝSPRAVKA KOMÍNA (LEPIACA MALTA+SKLOTEXTILNÁ MREŽKA+MOZAIKOVÁ OMIETKA)
- B2 - NOVÉ PODBITIE STRECHY OSB DOSKA HR. 25mm + TEPELNÁ IZOLÁCIA Z MINERÁLNEJ VLNY HR. 30mm SIEŤKA+LEPIDLO-POVRCHOVÁ ÚPRAVA SILIKÓNOVÁ OMIETKA
- S2 - MONTÁŽ NOVEJ KRYTINY, LATOVANIA, FÓLIE (VIĎ. SKLADBA STRECHY)
- P1 - REALIZÁCIA NOVÝCH PODLAHOVÝCH VRSTVIE (VIĎ. SKLADBY PODLÁH)
- P3 - REALIZÁCIA NOVÝCH NÁŠEAPNÝCH PODLAHOVÝCH VRSTVIE (VIĎ. SKLADBY PODLÁH)

LEGENDA MATERIÁLOV

- NOVÉ PRÁCE
NOVÉ PRÁCE
PÔVODNÁ KONŠTRUKCIA
TEPELNÁ IZOLÁCIA
RASTLÝ TERÉN

POZNÁMKA:

- #1 Tento dokument je originál a jeho kopírovanie je trestné.
#2 Všetky zmeny v projektoch treba prekonzultovať s HIP.
#3 Všetky rozmery je nutné domerať priamo na stavbe. Rozmery sú kótované bez ometok.

±0,000 = 487 m.n.m.

Názov stavby : **STAVEBNÉ ÚPRAVY MATERSKEJ ŠKOLY
V HORNOM VADIČOVE č.515**

LIMAT
REALITY & BUILDING

Generálny projektant : LIMAT Reality&Building, s.r.o.

Zodpovedný projektant : Ing. Miroslav Moravec
Vedúci projektant : Matúš Lipták
Vypracoval/a : Ing. Renáta Čavajdová

Investor : obec Horný Vadičov

Miesto stavby : obec Horný Vadičov | Okres : Kysucké nové Mesto
Kat. územie : Horný Vadičov | Parc. číslo : 1954/2


Časť : ARCH
Názov výkresu : **REZ A-A - NOVÝ STAV**

Dátum : 02 / 2024

Mierka : 1:100

Formát : 2xA4

Úroveň : DSP

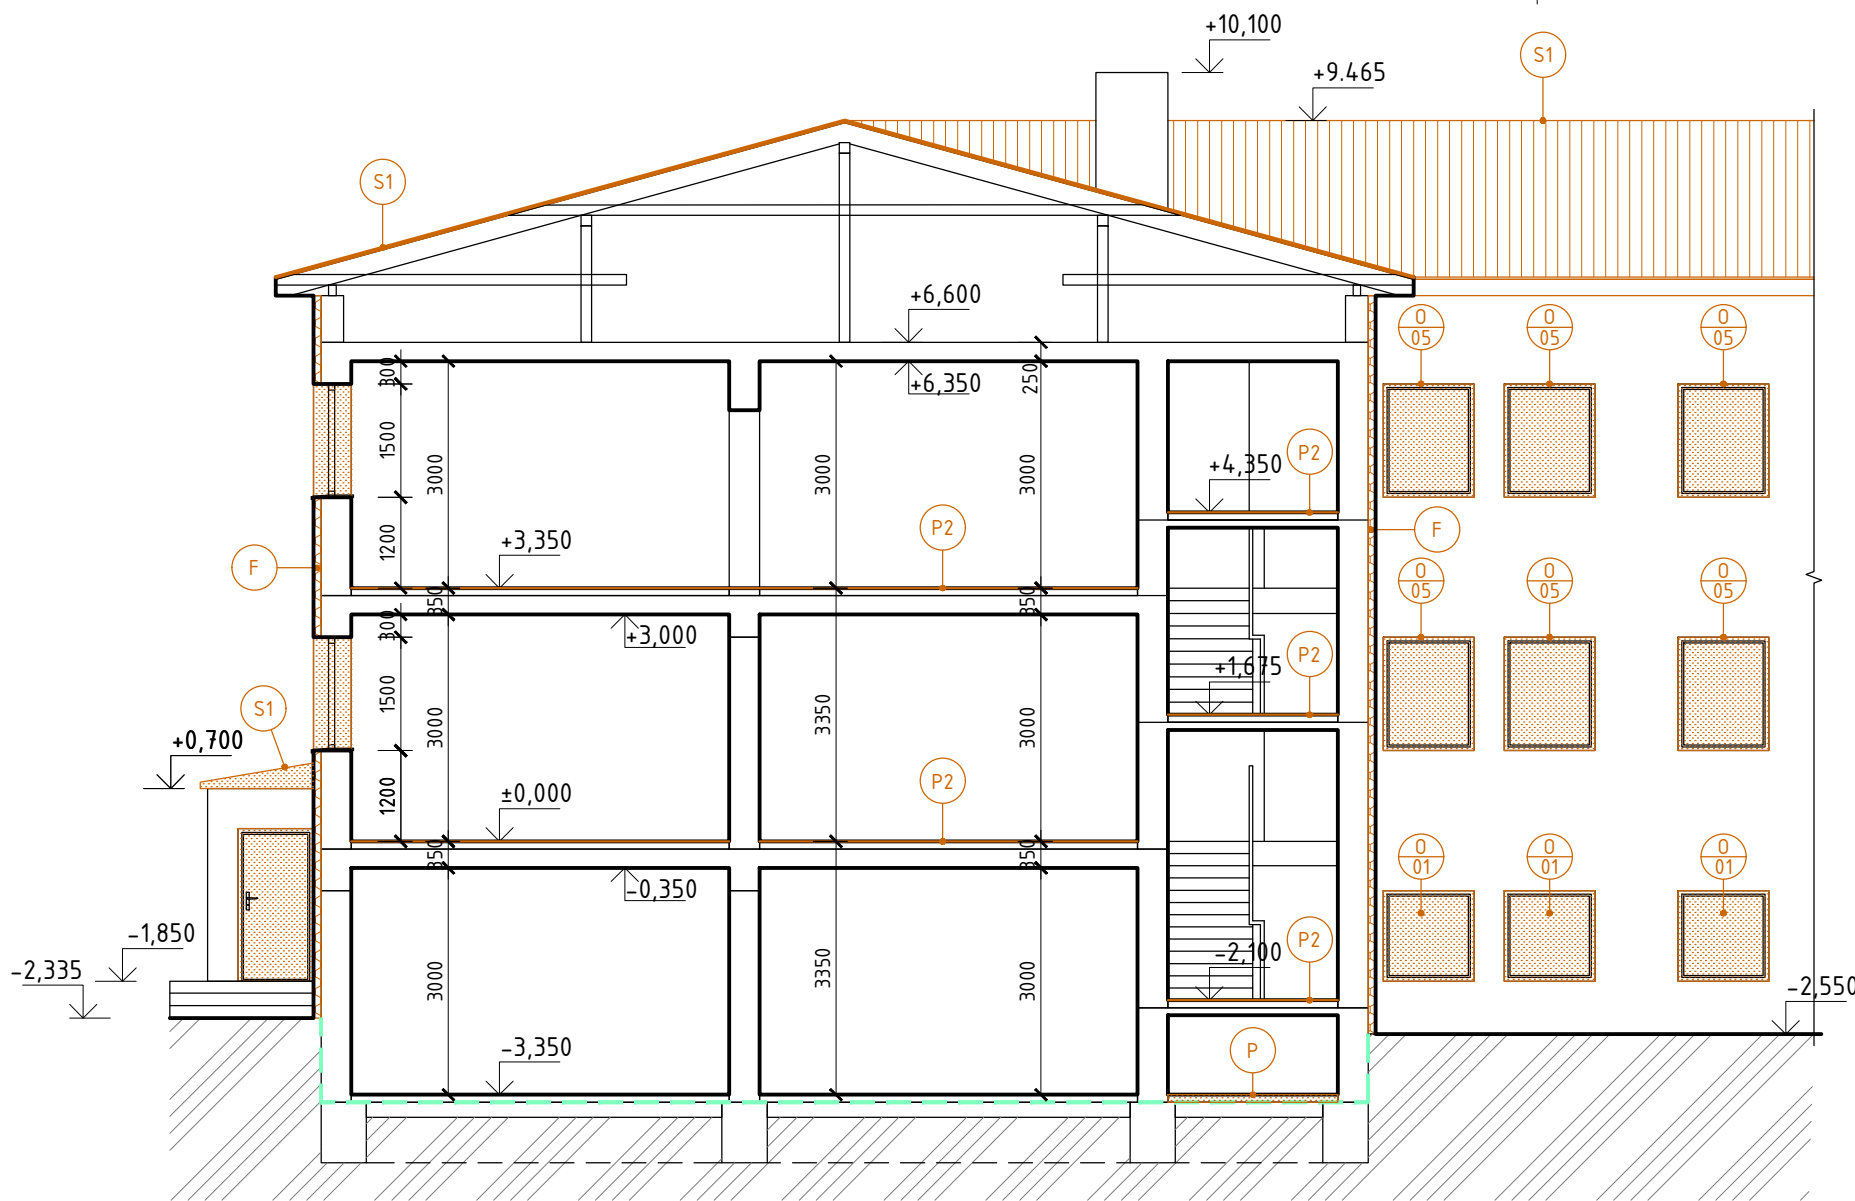

LEGENDA MATERIÁLOV

- BÚRACIE PRÁCE
- BÚRACIE PRÁCE
- PŮVODNÁ KONŠTRUKCIA
- TEPELNÁ IZOLÁCIA
- RASTLÝ TERÉN

LEGENDA

- F - PŮVODNÝ KONTAKTNÝ ZATEPLOVACÍ SYSTÉM - ZATEPLENIE FASÁDY, HRÚBKA 100mm
- O - DEMONTÁŽ PŮVODNÝCH OKIEN, INTERÉROVÝCH A EXTERIÉROVÝCH PARAPETOV
- D - DEMONTÁŽ PŮVODNÝCH DVERÍ
- Di - DEMONTÁŽ PŮVODNÝCH INT.DVERNÝCH KRÍDEL
- Z1 - DEMONTÁŽ PŮVODNÝCH PODODKVAPOVÝCH ŽLABOV, DAŽĎOVÝCH ZVODOV
- B1 - DEMONTÁŽ PŮVODNÉHO PODBITIA STRECHY
- S1 - DEMONTÁŽ PŮVODNEJ KRYTINY A LATOVANIA (VIĎ. SKLADBA STRECHY)
- P - ODSTRÁNENIE PŮVODNÝCH PODLAHOVÝCH VRSTVIEV PO ŽELEZOBET. DOSKU
- P2 - ODSTRÁNENIE PŮVODNÝCH NÁŠLAPNÝCH PODLAHOVÝCH VRSTVIEV

POZNÁMKA:

- #1 Tento dokument je originál a jeho kopírovanie je trestné.
- #2 Všetky zmeny v projektoch treba prekonzultovať s HIP.
- #3 Všetky rozmery je nutné domerať priamo na stavbe. Rozmery sú kótované bez omietok.

±0,000 = 487 m.n.m.

Názov stavby : **STAVEBNÉ ÚPRAVY MATERSKEJ ŠKOLY
V HORNOM VADIČOVE č.515**

LIMAT
REALITY & BUILDING

Generálny projektant : LIMAT Reality&Building, s.r.o.

Zodpovedný projektant : Vedúci projektant : Matúš Lipták
Ing. Miroslav Moravec Vypracoval/a : Ing. Renáta Čavajdová

Investor : obec Horný Vadičov

Miesto stavby : obec Horný Vadičov | Okres : Kysucké nové Mesto

Kat. územie : Horný Vadičov | Parc. číslo : 1954/2

Časť :
ARCH


Názov výkresu : **REZ A-A - STARÝ STAV**

Dátum : 02 / 2024

Mierka : 1:100

Formát : 2xA4

Úroveň : DSP

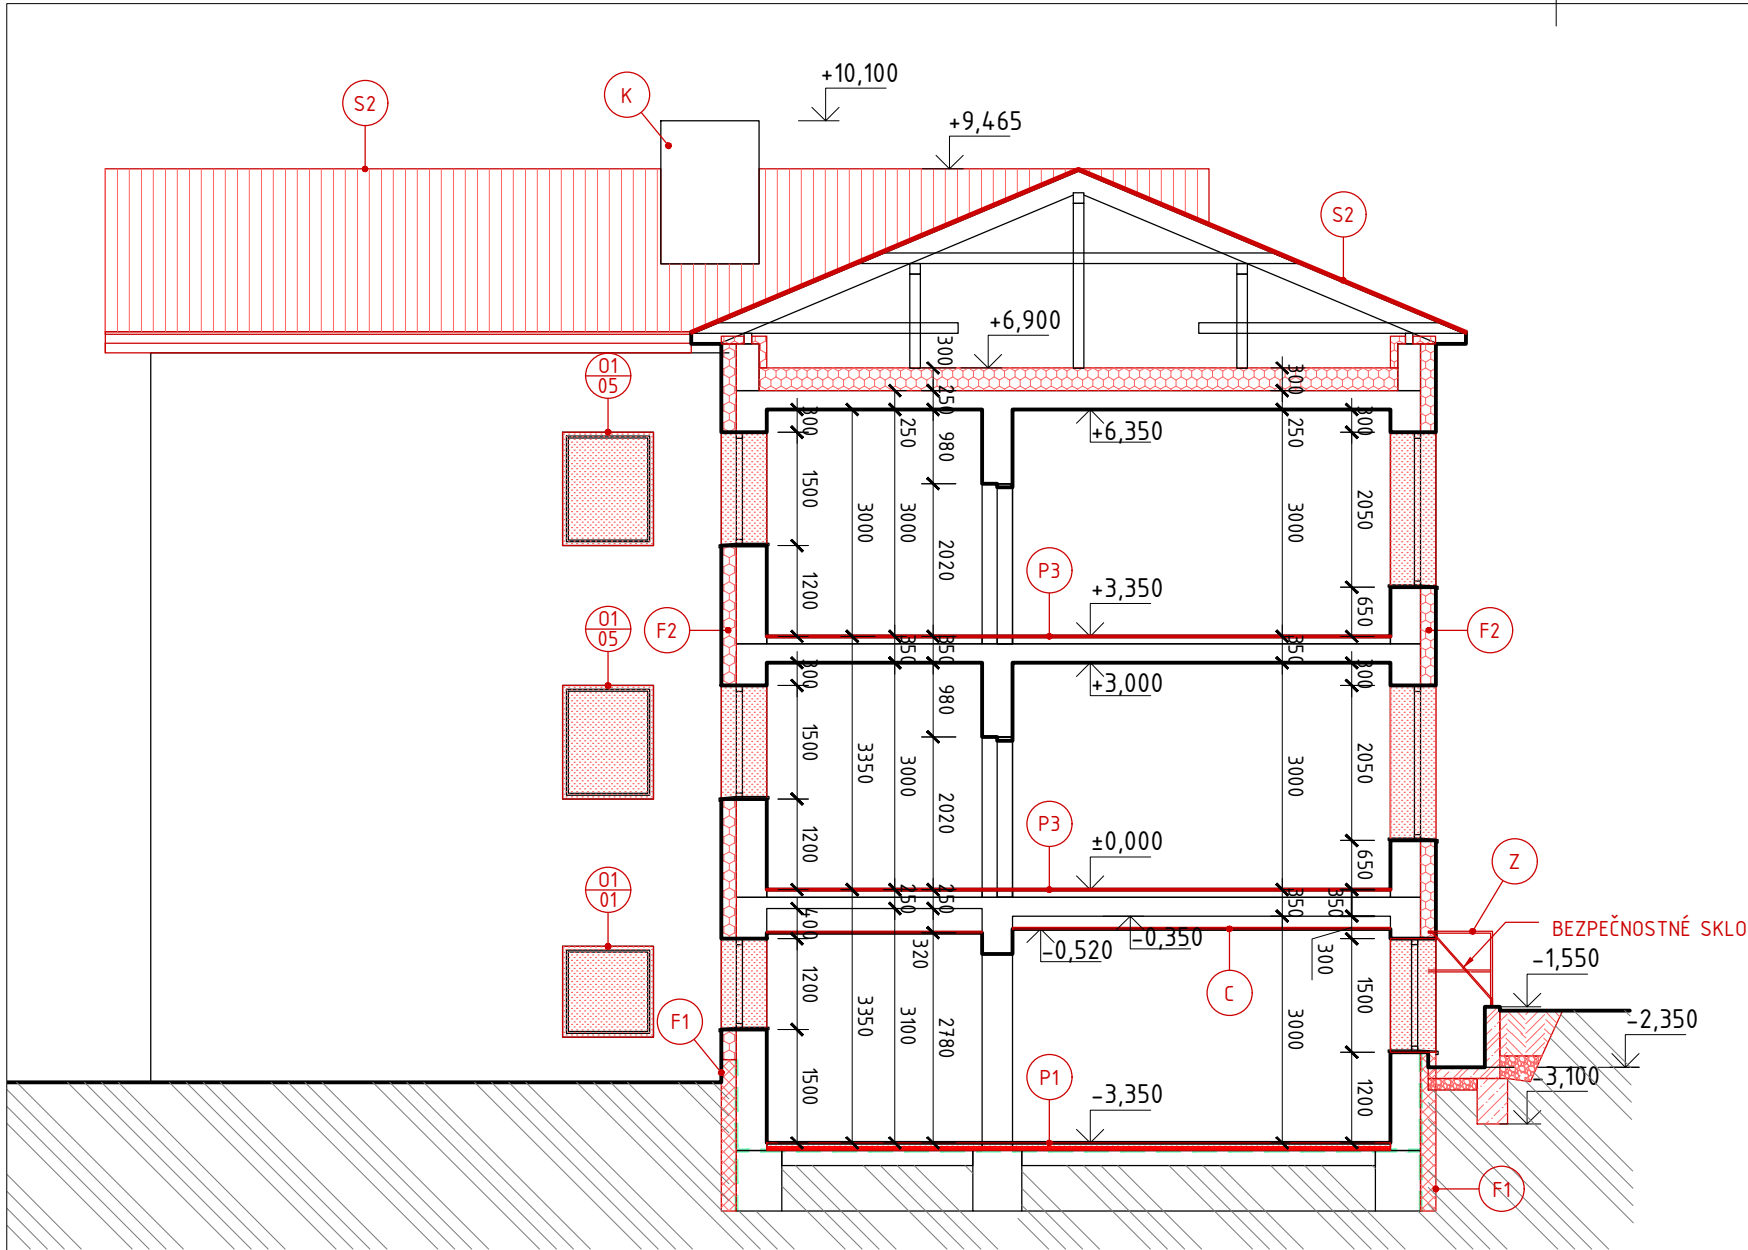

SKLADBY PODLÁH

- (P1) - NÁŠLAPNÁ VRSTVA 8mm
- PODLAHOVÉ LEPIDLO 2mm
- BET. POTER 40mm
- PODLAHOVÝ POLYSTYRÉN 50 mm
- PODKLADNÝ BETÓN
- RASTLÝ TERÉN

- (P3) - PVC LINOLEUM 2mm
- LEPIDLO POD PVC
- SAMONIVELIZAČNÝ POTER

SKLADBA STRECHY

- (S2) - FALCOVANÝ PLECH
- PAROZÁBRANA
- PLNÝ ZÁKLOP hr. 25mm
- KONTRALATY
- PAROPRIEPUSTNÁ FÓLIA
- PÔVODNÝ KROV

LEGENDA

- (F1) - CERTIFIKOVANÝ KONTAKTNÝ ZATEPLOVACÍ SYSTÉM (ETICS) V SOKLOVEJ ČASTI NA BÁZE XPS - IZOLANT DOSKY Z EXTRUDOVANÉHO POLYSTYRÉNU, HRÚBK 200mm
- V ČASTI NAD TERÉNOM ZHOTIVIŤ SIEŤKU+LEPIDLO+PENETRAČNÝ NÁTER, MARMOLIT
- SUTERÉNNE MURIVO OČISTIŤ, VYSPRAVIŤ (CCA 50%) A ZHOTIVIŤ NOVÚ HYDROIZOLAČNÚ VRSTVU 1xCEMIX 1K, SPOJENIE JESTVUJÚCEJ IZOLÁCIE S NOVOU STIERKOU DILATAČNÝM PÁSOM PODĽA TECH. LISTU VÝROBCU
- (F2) - CERTIFIKOVANÝ KONTAKTNÝ ZATEPLOVACÍ SYSTÉM NA BÁZE MINERÁLNEJ VLNY-ZATEPLENIE FASÁDY, HRÚBK 200mm, DEKLAROVANÝ SÚČINITEL TEPELNEJ VODIVOSTI (max. 0,035 W/(m.K)), POVRCHOVÁ ÚPRAVA - FAREBNÉ RIEŠENIE URČÍ INVEŠTOR
- (F3) - CERTIFIKOVANÝ KONTAKTNÝ ZATEPLOVACÍ SYSTÉM NA BÁZE MINERÁLNEJ VLNY-ZATEPLENIE OSTENÍ A NADPRAŽÍ OKIEN, VSTUPNÝCH DVERÍ, HRÚBK 30mm, DEKLAROVANÝ SÚČINITEL TEPELNEJ VODIVOSTI (max. 0,035 W/(m.K)), POVRCHOVÁ ÚPRAVA - FAREBNÉ RIEŠENIE URČÍ INVEŠTOR
- (01) - MONTÁŽ NOVÝCH OKIEN, INTERIEROVÝCH A EXTERIEROVÝCH PARAPETOV - PARAPRT POPLASTOVANÝ PLECH V ODTIENI PRÍSLUŠNÉHO OKNA (VIĎ. VÝPIS OKIEN A DVERÍ)
- (D1) - MONTÁŽ NOVÝCH DVERÍ (VIĎ. VÝPIS OKIEN A DVERÍ)
- (Di1) - MONTÁŽ NOVÝCH INT.DVERÍ (VIĎ. VÝPIS OKIEN A DVERÍ)
- (Z) - ZÁBRADLIE
- (Z2) - MONTÁŽ NOVÝCH PODODKVAPOVÝCH ŽLABOV, DAŽĎOVÝCH ZVODOV
- (C) - MONTÁŽ PLNÉHO SÁDROKARTÓNOVÉHO PODHLADU
- (K) - VÝSPRAVKA KOMÍNA (LEPIACA MALTA+SKLOTEXTILNÁ MREŽKA+MOZAIKOVÁ OMIETKA)
- (B2) - NOVÉ PODBITIE STRECHY OSB DOSKA HR. 25mm + TEPELNÁ IZOLÁCIA Z MINERÁLNEJ VLNY HR. 30mm SIEŤKA+LEPIDLO-POVRCHOVÁ ÚPRAVA SILIKÓNOVÁ OMIETKA
- (S2) - MONTÁŽ NOVEJ KRYTINY, LATOVANIA, FÓLIE (VIĎ. SKLADBA STRECHY)
- (P1) - REALIZÁCIA NOVÝCH PODLAHOVÝCH VRSTIEV (VIĎ. SKLADBY PODLÁH)
- (P3) - REALIZÁCIA NOVÝCH NÁŠLAPNÝCH PODLAHOVÝCH VRSTIEV (VIĎ. SKLADBY PODLÁH)

LEGENDA MATERIÁLOV

- NOVÉ PRÁCE
NOVÉ PRÁCE
PÔVODNÁ KONŠTRUKCIA
TEPELNÁ IZOLÁCIA
RASTLÝ TERÉN

POZNÁMKA:

- #1 Tento dokument je originál a jeho kopírovanie je trestné.
#2 Všetky zmeny v projektoch treba prekonzultovať s HIP.
#3 Všetky rozmery je nutné domerať priamo na stavbe. Rozmery sú kótované bez omietok.

±0,000 = 487 m.n.m.

Názov stavby : **STAVEBNÉ ÚPRAVY MATERSKEJ ŠKOLY
V HORNOM VADIČOVE č.515**

LIMAT
REALITY & BUILDING

Generálny projektant : LIMAT Reality&Building, s.r.o.

Zodpovedný projektant : Ing. Miroslav Moravec
Vedúci projektant : Matúš Lipták
Vypracoval/a : Ing. Renáta Čavajdová

Investor : obec Horný Vadičov

Miesto stavby : obec Horný Vadičov | Okres : Kysucké nové Mesto
Kat. územie : Horný Vadičov | Parc. číslo : 1954/2


Časť : ARCH
Názov výkresu : **REZ B-B - NOVÝ STAV**

Dátum : 02 / 2024

Mierka : 1:100

Formát : 2xA4

Úroveň : DSP

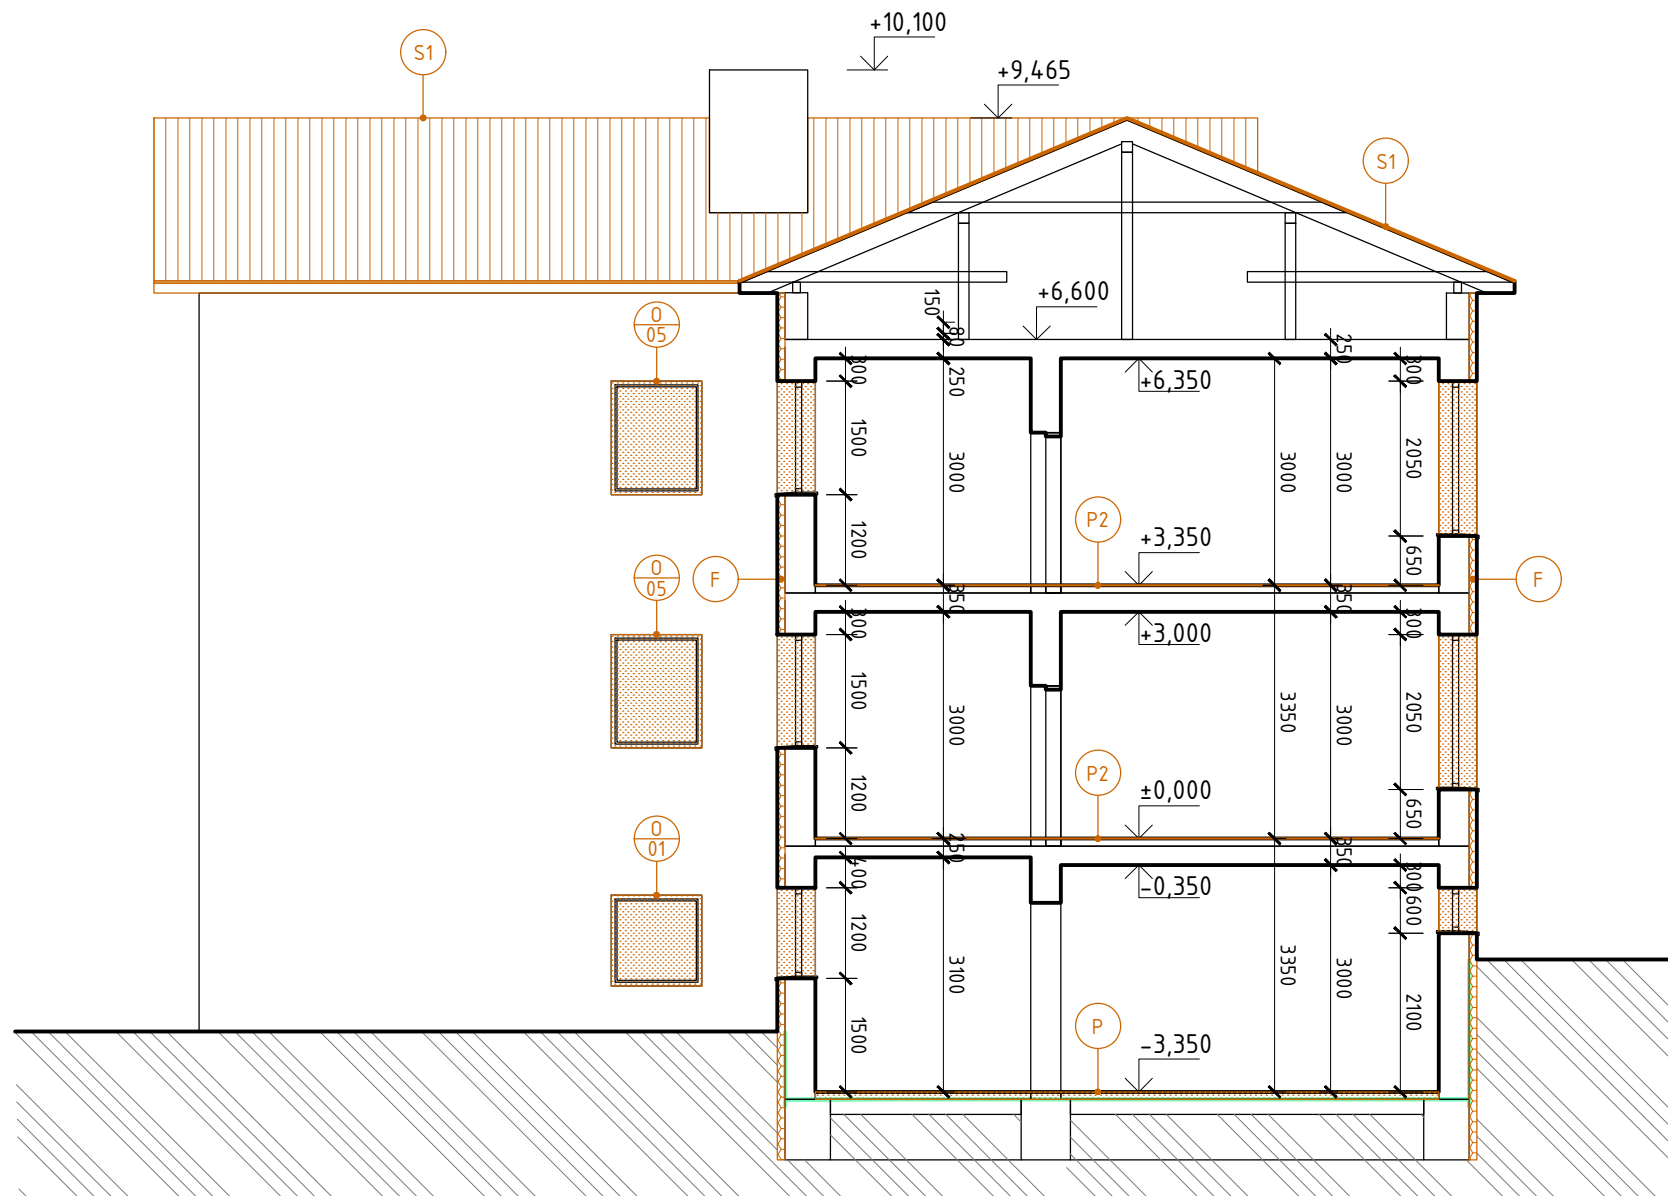

LEGENDA MATERIÁLOV

- BÚRACIE PRÁCE
- BÚRACIE PRÁCE
- PŮVODNÁ KONŠTRUKCIA
- TEPELNÁ IZOLÁCIA
- RASTLÝ TERÉN

LEGENDA

- F - PŮVODNÝ KONTAKTNÝ ZATEPLOVACÍ SYSTÉM - ZATEPLENIE FASÁDY, HRÚBKA 100mm
- O - DEMONTÁŽ PŮVODNÝCH OKIEN, INTERÉROVÝCH A EXTERIÉROVÝCH PARAPETOV
- D - DEMONTÁŽ PŮVODNÝCH DVERÍ
- Di - DEMONTÁŽ PŮVODNÝCH INT.DVERNÝCH KRÍDEL
- Z1 - DEMONTÁŽ PŮVODNÝCH PODODKVAPOVÝCH ŽĽABOV, DAŽĎOVÝCH ZVODOV
- B1 - DEMONTÁŽ PŮVODNÉHO PODBITIA STRECHY
- S1 - DEMONTÁŽ PŮVODNEJ KRYTINY A LATOVANIA (VIĎ. SKLADBA STRECHY)
- P - ODSTRÁNENIE PŮVODNÝCH PODLAHOVÝCH VRSTVIE PO ŽELEZOBET. DOSKU
- P2 - ODSTRÁNENIE PŮVODNÝCH NÁŠČAPNÝCH PODLAHOVÝCH VRSTVIE

POZNÁMKA:

#1 Tento dokument je originál a jeho kopírovanie je trestné.

#2 Všetky zmeny v projektoch treba prekonzultovať s HIP.

#3 Všetky rozmery je nutné domerať priamo na stavbe. Rozmery sú kótované bez omietok.

±0,000 = 487 m.n.m.

Názov stavby : **STAVEBNÉ ÚPRAVY MATERSKEJ ŠKOLY
V HORNOM VADIČOVE č.515**

LIMAT
REALITY & BUILDING

Generálny projektant : LIMAT Reality&Building, s.r.o.

Zodpovedný projektant :

Ing. Miroslav Moravec

Vedúci projektant : Matúš Lipták

Vypracoval/a : Ing. Renáta Čavajdová

Investor :

obec Horný Vadičov

Dátum : 02 / 2024

Mierka : 1:100

Miesto stavby : obec Horný Vadičov

Okres : Kysucké nové Mesto

Formát : 2xA4

Kat. územie : Horný Vadičov

Parc. číslo : 1954/2

Úroveň : DSP

Časť :

ARCH

Názov výkresu :

REZ B-B - STARÝ STAV